

AERODROME CHART - ICAO

52°25'16" N
016°49'35" E

ELEV 309 ft
GEOID UND. 115 ft

Poznań GROUND 124.140
Poznań DELIVERY 121.805

Poznań TOWER 119.980
ATIS 124.705

Poznań - Ławica

GEOGRAPHICAL
COORDINATES FOR
APPROPRIATE TAXIWAY
CENTRE LINE POINTS

TWY D2		
Nr	LATITUDE	LONGITUDE
61	52°25'07.83"N	16°49'43.53"E
101	52°25'07.46"N	16°49'45.45"E
151	52°25'07.95"N	16°49'42.93"E
371	52°25'25.65"N	16°48'20.09"E
381	52°25'23.62"N	16°48'21.82"E
441	52°25'19.58"N	16°48'42.74"E
461	52°25'20.97"N	16°48'35.51"E
P386	52°25'27.47"N	16°48'21.03"E
P837	52°25'28.10"N	16°48'21.35"E
P847	52°25'29.18"N	16°48'22.89"E
P853	52°25'29.20"N	16°48'24.82"E
P854	52°25'28.65"N	16°48'27.64"E
D2	52°25'26.95"N	16°48'20.76"E

TWY D1		
Nr	LATITUDE	LONGITUDE
81	52°25'07.09"N	16°49'47.37"E
171	52°25'06.97"N	16°49'47.97"E
191	52°25'00.39"N	16°50'22.03"E
251	52°25'00.35"N	16°50'22.22"E

TWY S		
Nr	LATITUDE	LONGITUDE
43/2	52°25'21.76"N	16°48'42.84"E
44/2	52°25'19.58"N	16°48'42.74"E

ATWY L		
46/2	52°25'20.97"N	16°48'35.51"E
47/2	52°25'20.94"N	16°48'36.81"E
201/2	52°25'22.36"N	16°48'47.30"E
P628	52°25'22.41"N	16°48'47.68"E

ATWY M		
P637	52°25'22.76"N	16°48'55.00"E
P643	52°25'22.05"N	16°49'01.82"E
P644	52°25'21.34"N	16°49'05.48"E
S	52°25'22.00"N	16°48'44.57"E

TWY R		
Nr	LATITUDE	LONGITUDE
28/5	52°25'02.17"N	16°50'12.81"E
29/5	52°25'04.01"N	16°50'14.73"E

TWY N 1		
Nr	LATITUDE	LONGITUDE
30/5	52°25'02.91"N	16°50'15.13"E
31/5	52°25'01.49"N	16°50'16.34"E
P677	52°25'05.73"N	16°50'12.16"E
P684	52°25'08.76"N	16°50'06.56"E
P690	52°25'10.81"N	16°49'59.96"E
P693	52°25'11.60"N	16°49'55.91"E

TWY F		
Nr	LATITUDE	LONGITUDE
300	52°25'04.78"N	16°49'44.06"E
301	52°25'04.10"N	16°49'42.45"E
303	52°25'02.87"N	16°49'43.07"E
304	52°25'02.90"N	16°49'43.09"E

TWY N 2		
Nr	LATITUDE	LONGITUDE
305	52°25'04.13"N	16°49'41.65"E
307	52°25'04.15"N	16°49'41.10"E
308	52°25'04.20"N	16°49'39.71"E
315	52°25'04.30"N	16°49'37.06"E
320	52°25'04.40"N	16°49'34.47"E

TWY G		
Nr	LATITUDE	LONGITUDE
338	52°25'00.21"N	16°49'34.96"E
342	52°25'00.19"N	16°49'35.52"E
357	52°25'00.07"N	16°49'38.62"E
362	52°25'00.02"N	16°49'40.00"E
371	52°24'59.78"N	16°49'43.59"E
376	52°24'59.66"N	16°49'44.44"E
387	52°24'59.87"N	16°49'42.91"E
388	52°24'59.95"N	16°49'42.07"E
607	52°24'56.64"N	16°50'06.40"E
608	52°24'56.51"N	16°50'07.90"E
610	52°24'56.17"N	16°50'18.07"E
611	52°24'56.54"N	16°50'19.70"E

TWY T		
Nr	LATITUDE	LONGITUDE
DKGII	52°24'58.27"N	16°50'22.79"E


TWY A		
Nr	LATITUDE	LONGITUDE
613	52°24'58.96"N	16°50'23.41"E
P246	52°25'01.51"N	16°50'24.97"E
P742	52°25'06.66"N	16°50'21.42"E
P749	52°25'06.02"N	16°50'24.71"E
P785	52°25'03.98"N	16°50'26.46"E
A	52°25'02.52"N	16°50'25.58"E

TWY B		
Nr	LATITUDE	LONGITUDE
P867	52°25'14.15"N	16°49'42.69"E
P869	52°25'13.57"N	16°49'45.70"E
P873	52°25'12.76"N	16°49'47.38"E
P879	52°25'11.54"N	16°49'47.56"E
P886	52°25'12.56"N	16°49'49.18"E
P891	52°25'12.56"N	16°49'50.92"E
P893	52°25'11.97"N	16°49'53.98"E
P910	52°25'09.91"N	16°49'46.71"E

TWY W		
Nr	LATITUDE	LONGITUDE
P212	52°25'29.20"N	16°50'33.67"E
P235	52°25'28.90"N	16°50'34.68"E
P238	52°25'28.57"N	16°50'35.79"E
P261	52°25'28.22"N	16°50'36.98"E
P402	52°25'29.69"N	16°50'32.02"E
P403	52°25'30.01"N	16°50'30.93"E
P404	52°25'30.05"N	16°50'30.76"E
P405	52°25'30.06"N	16°50'30.69"E

TWY Y		
Nr	LATITUDE	LONGITUDE
X5	52°25'27.79"N	16°50'38.42"E
X7	52°25'08.63"N	16°49'46.06"E
9	52°25'06.29"N	16°49'44.84"E
18	52°25'05.92"N	16°49'44.65"E
325	52°25'01.75"N	16°49'42.49"E
B	52°25'10.05"N	16°49'46.78"E
DKBII	52°25'05.92"N	16°49'44.65"E

LEGEND					
AIRCRAFT STAND					• 1
RUNWAY / TAXIWAY EDGE LIGHT					◦
TAXIWAY EDGE MARKER					•
TAXIWAY CENTRE LIGHT					◦
TAXIWAY CENTRE LINE MARKER					•
FLASHING LIGHT					⋈
APRON LIGHT					⋈
ATC SERVICE BOUNDARY					⋈
POLE, TOWER, SPIRE, ANTENNA, ETC.					⊙
TAXI - HOLDING POSITION					⋈
NO ENTRY FOR THE INDICATED DIRECTION					⋈
LIGHTING				BEARING STRENGTH	
RWY No	APCH	THR	RWY	END	RWY: see AD2 EPPO point 2.12 TWYs: see AD2 EPPO point 2.8
28	W LIH	G LIH	W/Y LIH	RED	
10	W LIH	G LIH	W/Y LIH	RED	

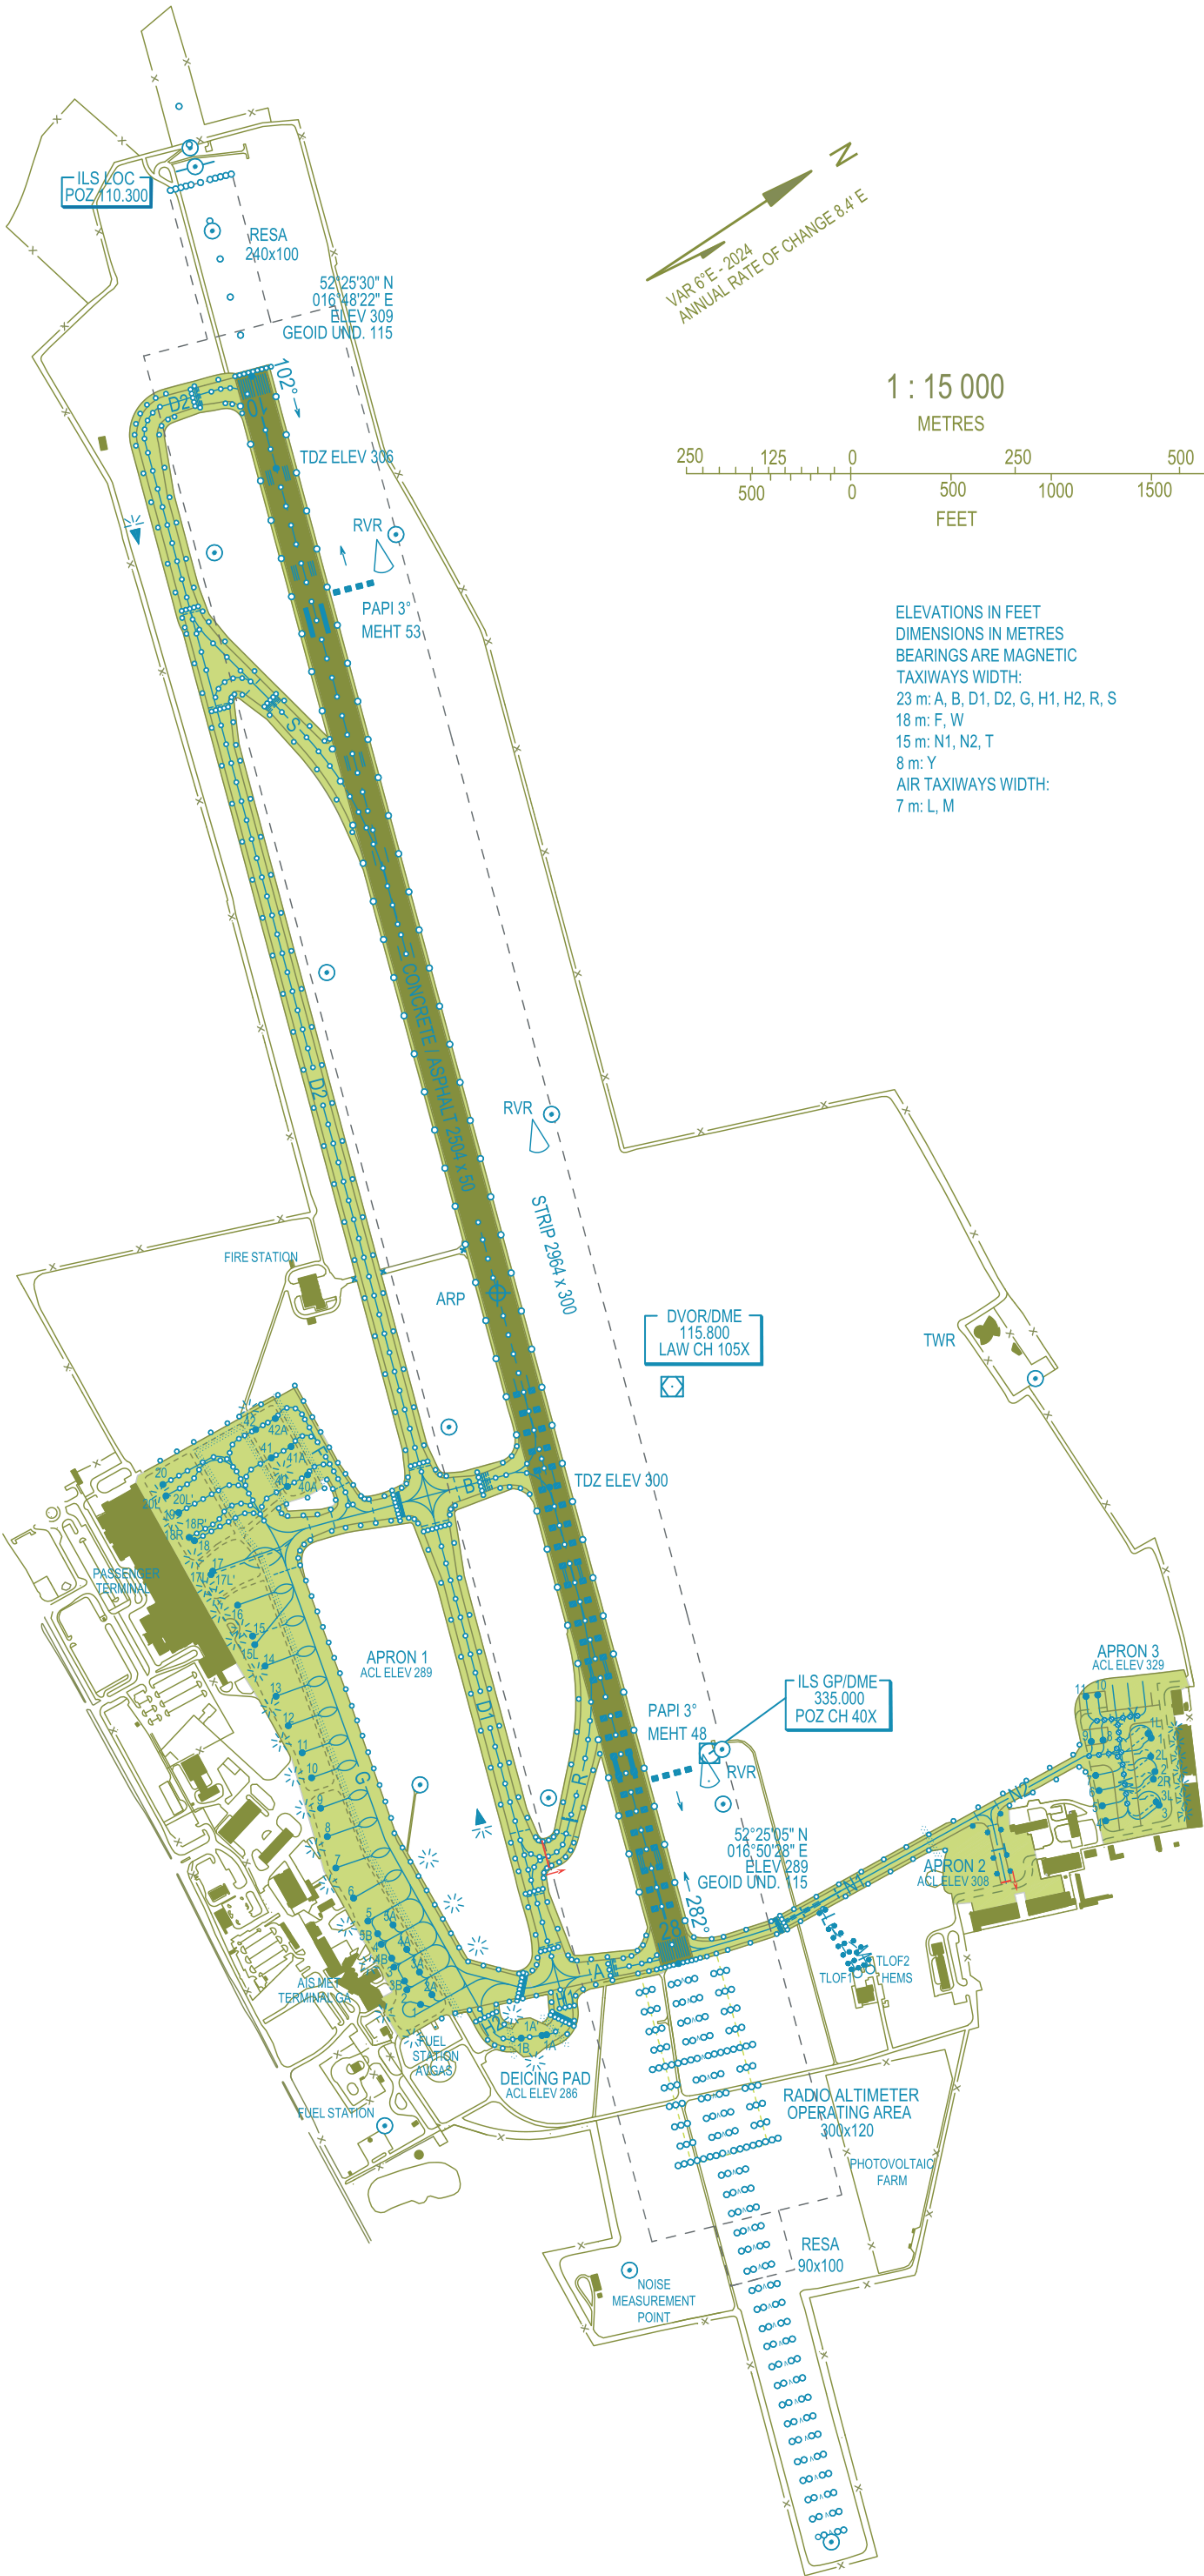

ELEVATIONS IN FEET
DIMENSIONS IN METRES
BEARINGS ARE MAGNETIC
TAXIWAYS WIDTH:
23 m: A, B, D1, D2, G, H1, H2, R, S
18 m: F, W
15 m: N1, N2, T
8 m: Y
AIR TAXIWAYS WIDTH:
7 m: L, M

Hand Amdt correction:
Correction: Page number changed.
Correction: VAR changed